


FRONT ELEVATION

DOUG JONES · 123 MAIN ST, PITTSBURGH, PA 15215 · SHEET EL-1 OF 4

NOT A SURVEY — SOURCE-TAGGED VERIFICATION SHEET

LINEWORK = COMPONENT · CHIPS = SOURCE

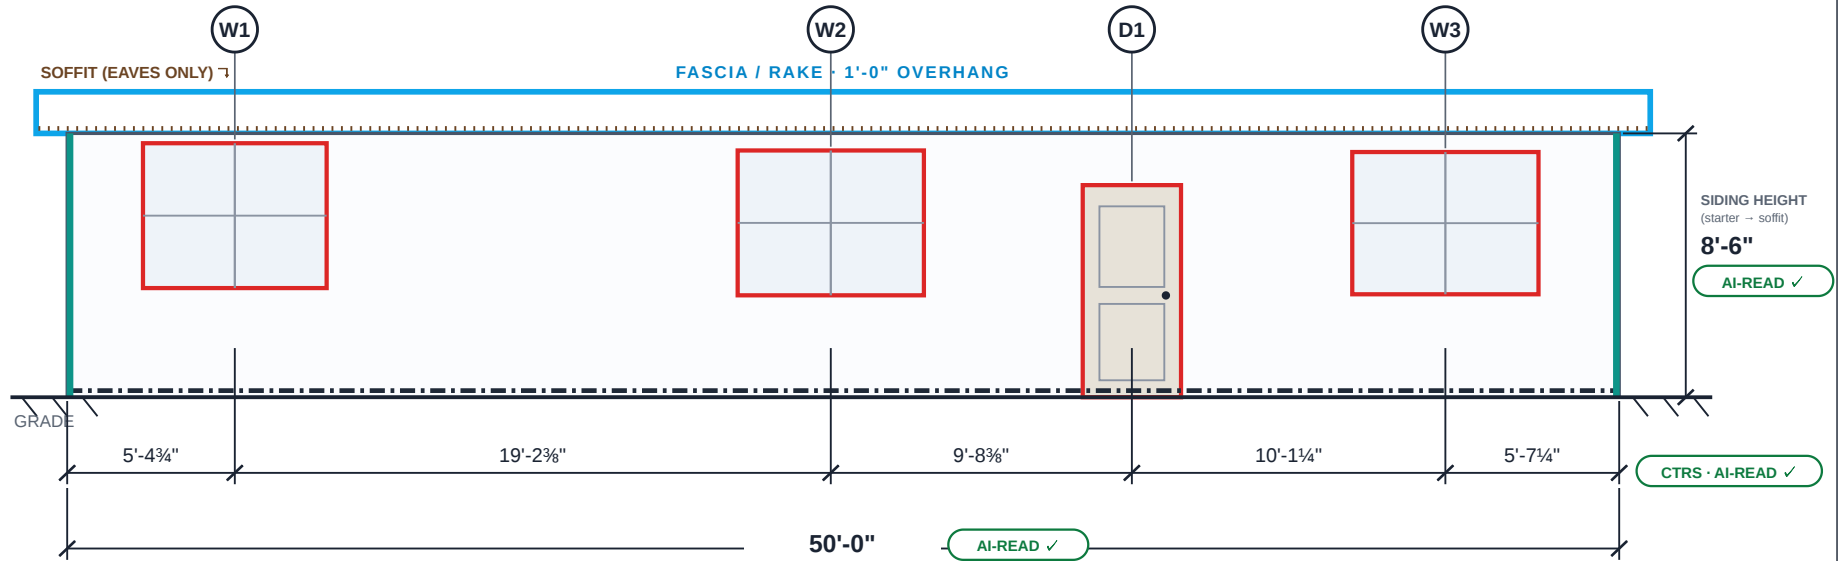

WALL DATA — FRONT

Width **50'-0"** — AI-READ ✓ (AI run (direct_ref))

Siding height (starter → soffit) **8'-6"** — AI-READ ✓ (AI run (direct_consensus))

Wall area **425 ft²** — DERIVED (50 × 8.5) · Gable triangle **none** · Stories 1

Siding **92%** · Profile callout **LAP 4"**

Openings **4** (3 windows · 1 entry door · 0 vents) — positions AI-READ ✓

AI source photos: 0, 1, 7 · AI confidence 88

OPENING SCHEDULE — FRONT

TAG	TYPE / STYLE	SIZE (W×H)	CTR @	SILL
W1	Window · Twin Single Hung	71×56 in	5'-4¾"	3'-6¼"
W2	Window · Twin Single Hung	72×56 in	24'-7¼"	3'-3¾"
D1	Entry door	38×82 in	34'-3¾"	0'-0"
W3	Window · Twin Single Hung	72×55 in	44'-4¾"	3'-3¾"

Swatch = drawn element's component class (opening trim).

Sizes + positions: AI run (along_wall_ft). Sills: photo bbox, door-anchored (doors at grade).


DOUG JONES	SHEET EL-1 · FRONT
GEOMETRY BASIS: AI run 0044b4c2... — walls openings: AI run 0044b4c2...e2 (claude-fable-5, 2026-07-14)	
Scale ≈ 5/32" = 1'-0" (auto-fit)	Pro-Quote · 2026-07-20
KEY — LINEWORK = COMPONENT · CHIPS = SOURCE	
— SIDING — TRIM — OSC — ISC — FASCIA/RAKE	
... SOFFIT — STARTER — BAND BD (C-SPEC)	
TAPED	T-DER
AI ✓	AI △
EST	PRINT
USER	C-SPEC

LEFT ELEVATION

DOUG JONES · 123 MAIN ST, PITTSBURGH, PA 15215 · SHEET EL-2 OF 4

NOT A SURVEY — SOURCE-TAGGED VERIFICATION SHEET

LINEWORK = COMPONENT · CHIPS = SOURCE

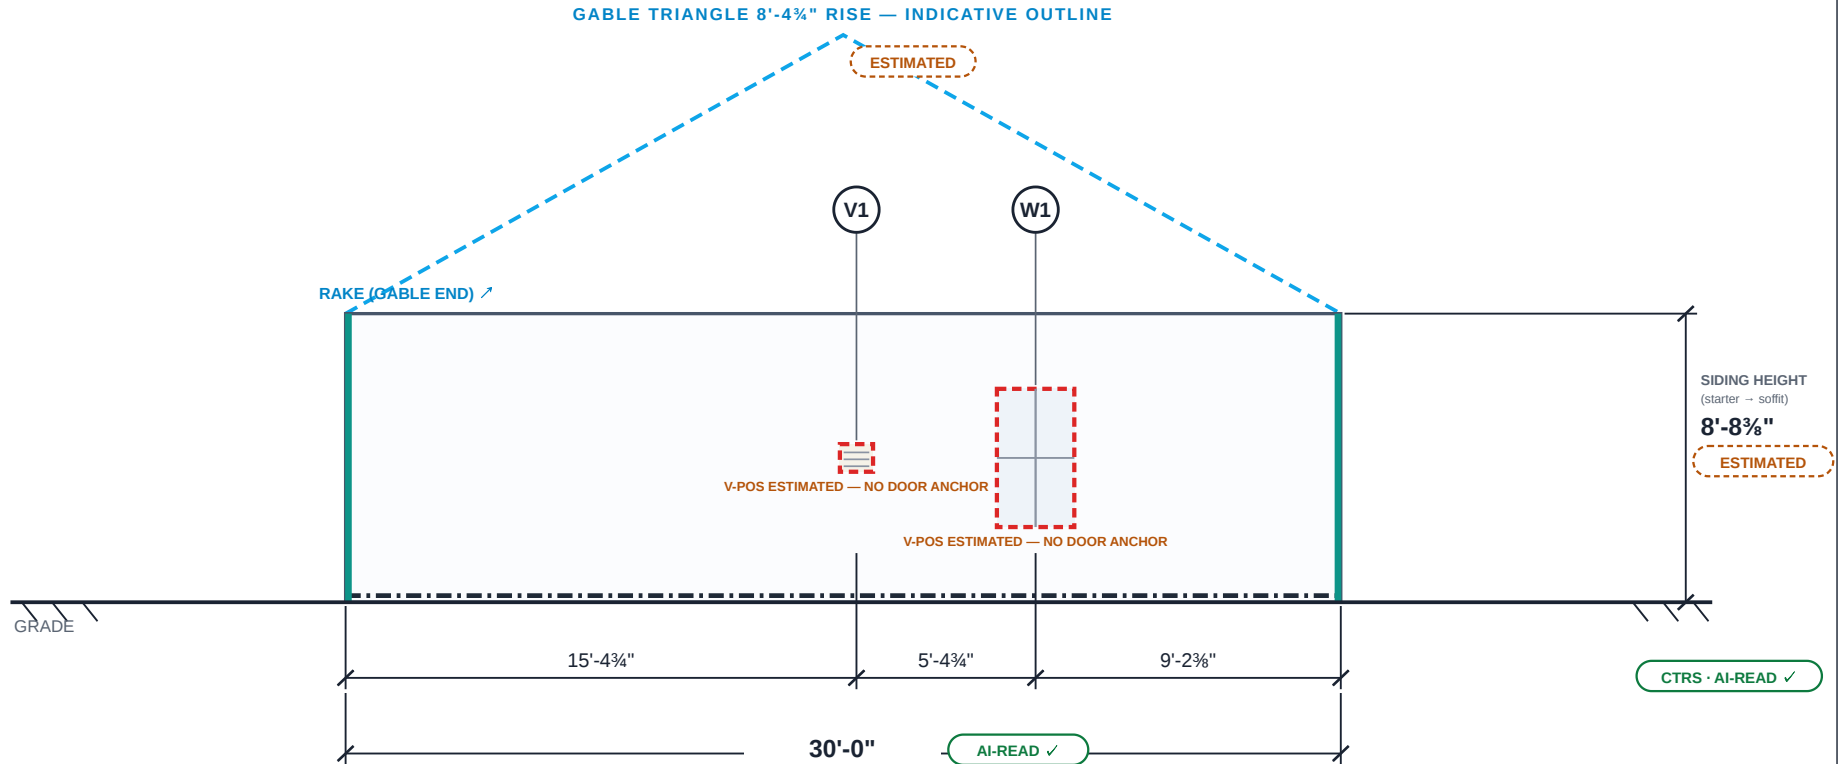

WALL DATA — LEFT

Width 30'-0" — AI-READ ✓ (AI run (direct_ref))

Siding height (starter → soffit) 8'-8 3/8" — ESTIMATED (AI run (estimated_no_direct_view))

Wall area 261 ft² — DERIVED (30 × 8.7) · Gable triangle 8'-4 3/4" [ESTIMATED] · Stories 1

Siding 97% · Profile callout LAP 4"

Openings 2 (1 windows · 0 entry doors · 1 vent) — positions AI-READ ✓

AI source photos: 2, 1, 3 · AI confidence 60

OPENING SCHEDULE — LEFT

TAG	TYPE / STYLE	SIZE (W×H)	CTR @	SILL
V1	Vent	12×10 in	15'-4 3/4"	—
W1	Window · DH	28×50 in	20'-9 5/8"	—

Swatch = drawn element's component class (opening trim).

Sizes + positions: AI run (along_wall_ft). Sills: photo bbox, door-anchored (doors at grade).


DOUG JONES	SHEET EL-2 · LEFT
GEOMETRY BASIS: AI run 0044b4c2... — walls openings: AI run 0044b4c2...e2 (claude-fable-5, 2026-07-14)	
Scale ≈ 3/16" = 1'-0" (auto-fit)	Pro-Quote · 2026-07-20
KEY — LINEWORK = COMPONENT · CHIPS = SOURCE	
— SIDING	— TRIM
— OSC	— ISC
— SOFFIT	— BAND BD (C-SPEC)
— FASCIA/RAKE	
TAPED	T-DER
AI ✓	AI △
EST	PRINT
USER	C-SPEC

BACK ELEVATION

DOUG JONES · 123 MAIN ST, PITTSBURGH, PA 15215 · SHEET EL-3 OF 4

NOT A SURVEY — SOURCE-TAGGED VERIFICATION SHEET

LINEWORK = COMPONENT · CHIPS = SOURCE

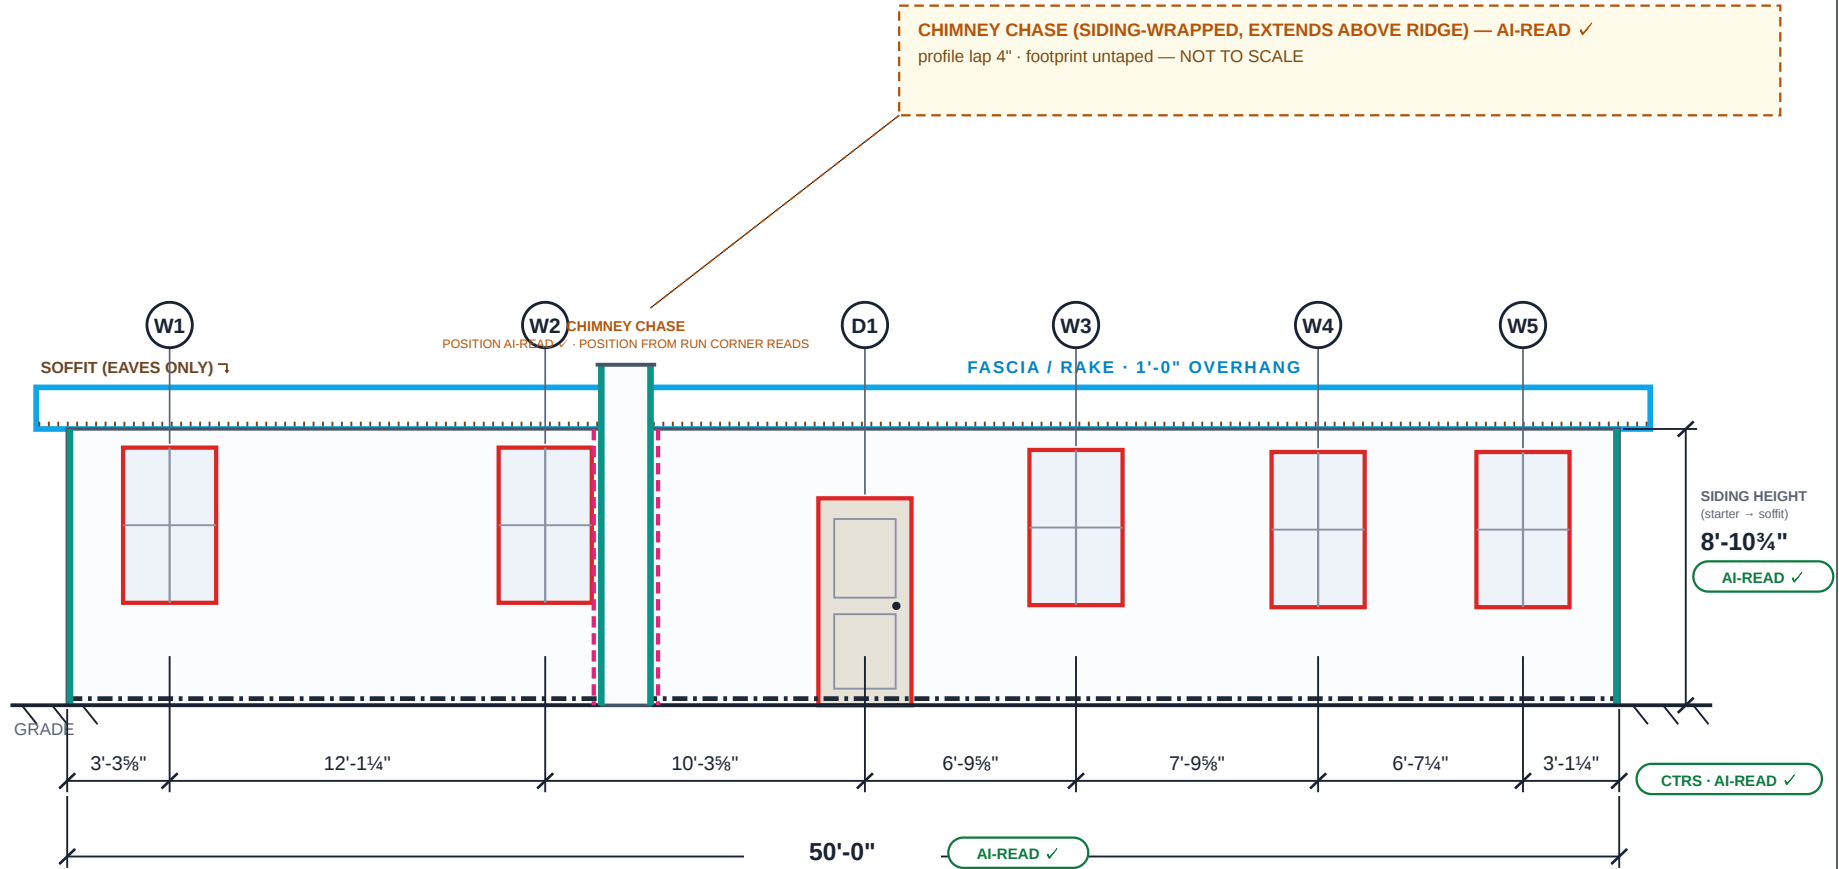

WALL DATA — BACK

Width 50'-0" — AI-READ ✓ (AI run (direct_ref))

Siding height (starter → soffit) 8'-10 1/4" — AI-READ ✓ (AI run (direct_consensus))

Wall area 445 ft² — DERIVED (50 × 8.9) · Gable triangle none · Stories 1

Siding 92% · Profile callout LAP 4"

Openings 6 (5 windows · 1 entry door · 0 vents) — positions AI-READ ✓

AI source photos: 4, 3, 5 · AI confidence 85

OPENING SCHEDULE — BACK

TAG	TYPE / STYLE	SIZE (W×H)	CTR @	SILL
W1	Window · Single Hung	36×60 in	3'-3 3/8"	3'-3 3/8"
W2	Window · Single Hung	36×60 in	15'-4 3/4"	3'-3 3/8"
D1	Entry door	36×80 in	25'-8 3/8"	0'-0"
W3	Window · Single Hung	36×60 in	32'-6"	3'-2 3/4"
W4	Window · Single Hung	36×60 in	40'-3 3/8"	3'-1 1/8"
W5	Window · Single Hung	36×60 in	46'-10 3/4"	3'-1 1/8"

Swatch = drawn element's component class (opening trim).

Sizes + positions: AI run (along_wall_ft). Sills: photo bbox, door-anchored (doors at grade).

DOUG JONES

SHEET EL-3 · BACK

GEOMETRY BASIS: AI run 0044b4c2... — walls
openings: AI run 0044b4c2...e2 (claude-fable-5, 2026-07-14)

Scale ≈ 5/32" = 1'-0" (auto-fit)

Pro-Quote · 2026-07-20

KEY — LINEWORK = COMPONENT · CHIPS = SOURCE

— SIDING — TRIM — OSC — ISC — FASCIA/RAKE

· · · SOFFIT — — STARTER — — BAND BD (C-SPEC)


TAPED T-DER AI ✓ AI △ EST PRINT USER C-SPEC

RIGHT ELEVATION

DOUG JONES · 123 MAIN ST, PITTSBURGH, PA 15215 · SHEET EL-4 OF 4

NOT A SURVEY — SOURCE-TAGGED VERIFICATION SHEET

LINEWORK = COMPONENT · CHIPS = SOURCE

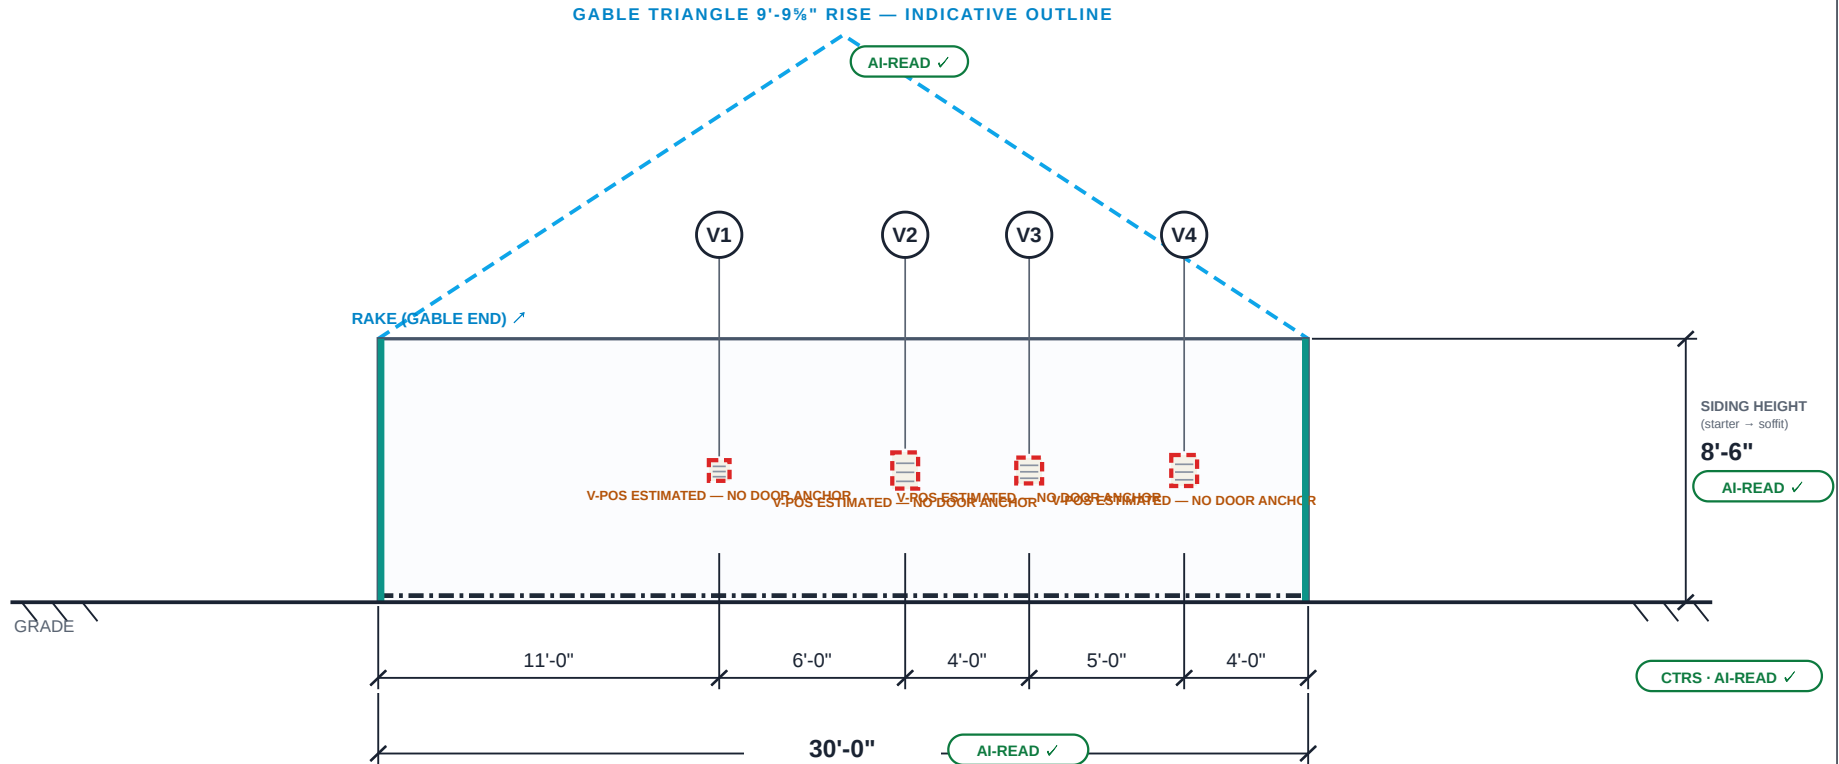

WALL DATA — RIGHT

Width 30'-0" — AI-READ ✓ (AI run (direct_ref))

Siding height (starter → soffit) 8'-6" — AI-READ ✓ (AI run (direct_single_reading))

Wall area 255 ft² — DERIVED (30 × 8.5) · Gable triangle 9'-9 1/2" [AI-READ ✓] · Stories 1

Siding 99% · Profile callout LAP 4"

Openings 4 (0 windows · 0 entry doors · 4 vents) — positions AI-READ ✓

AI source photos: 7, 6, 5 · AI confidence 70

OPENING SCHEDULE — RIGHT

TAG	TYPE / STYLE	SIZE (W×H)	CTR @	SILL
V1	Vent	8×8 in	11'-0"	—
V2	Vent	10×14 in	17'-0"	—
V3	Vent	10×10 in	21'-0"	—
V4	Vent	10×12 in	26'-0"	—

Swatch = drawn element's component class (opening trim).

Sizes + positions: AI run (along_wall_ft). Sills: photo bbox, door-anchored (doors at grade). No door on this wall — sills not derivable (—).

DOUG JONES

SHEET EL-4 · RIGHT

GEOMETRY BASIS: AI run 0044b4c2... — walls
openings: AI run 0044b4c2...e2 (claude-fable-5, 2026-07-14)

Scale = 5/32" = 1'-0" (auto-fit)

Pro-Quote · 2026-07-20

KEY — LINEWORK = COMPONENT · CHIPS = SOURCE

— SIDING — TRIM — OSC — ISC — FASCIA/RAKE

... SOFFIT — STARTER — BAND BD (C-SPEC)

TAPED T-DER AI ✓ AI △ EST PRINT USER C-SPEC